



# Campus Cafeteria


- Kitchen - Expansion/ New Equipment
- Kitchen - Expansion/ No New Equipment
- Servery - Area of Improvement
- Indoor Dining
- Covered Patio Dining

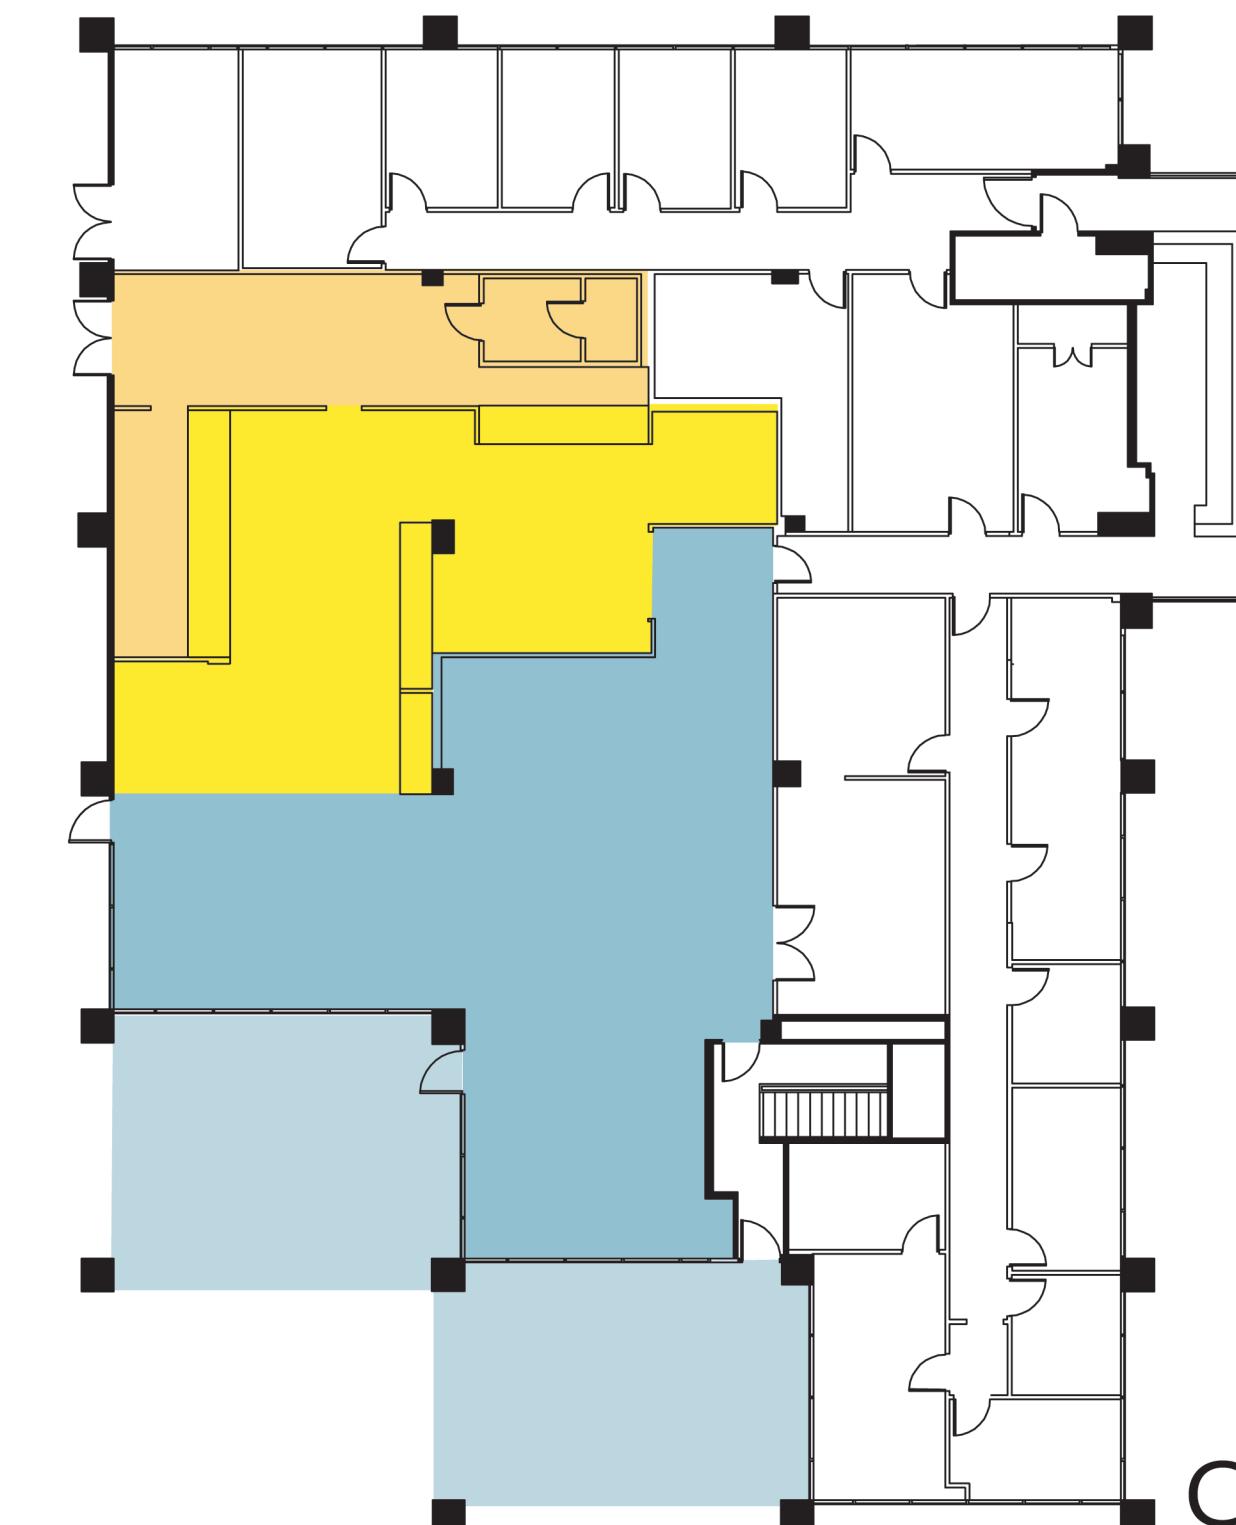


Current Floor Plan

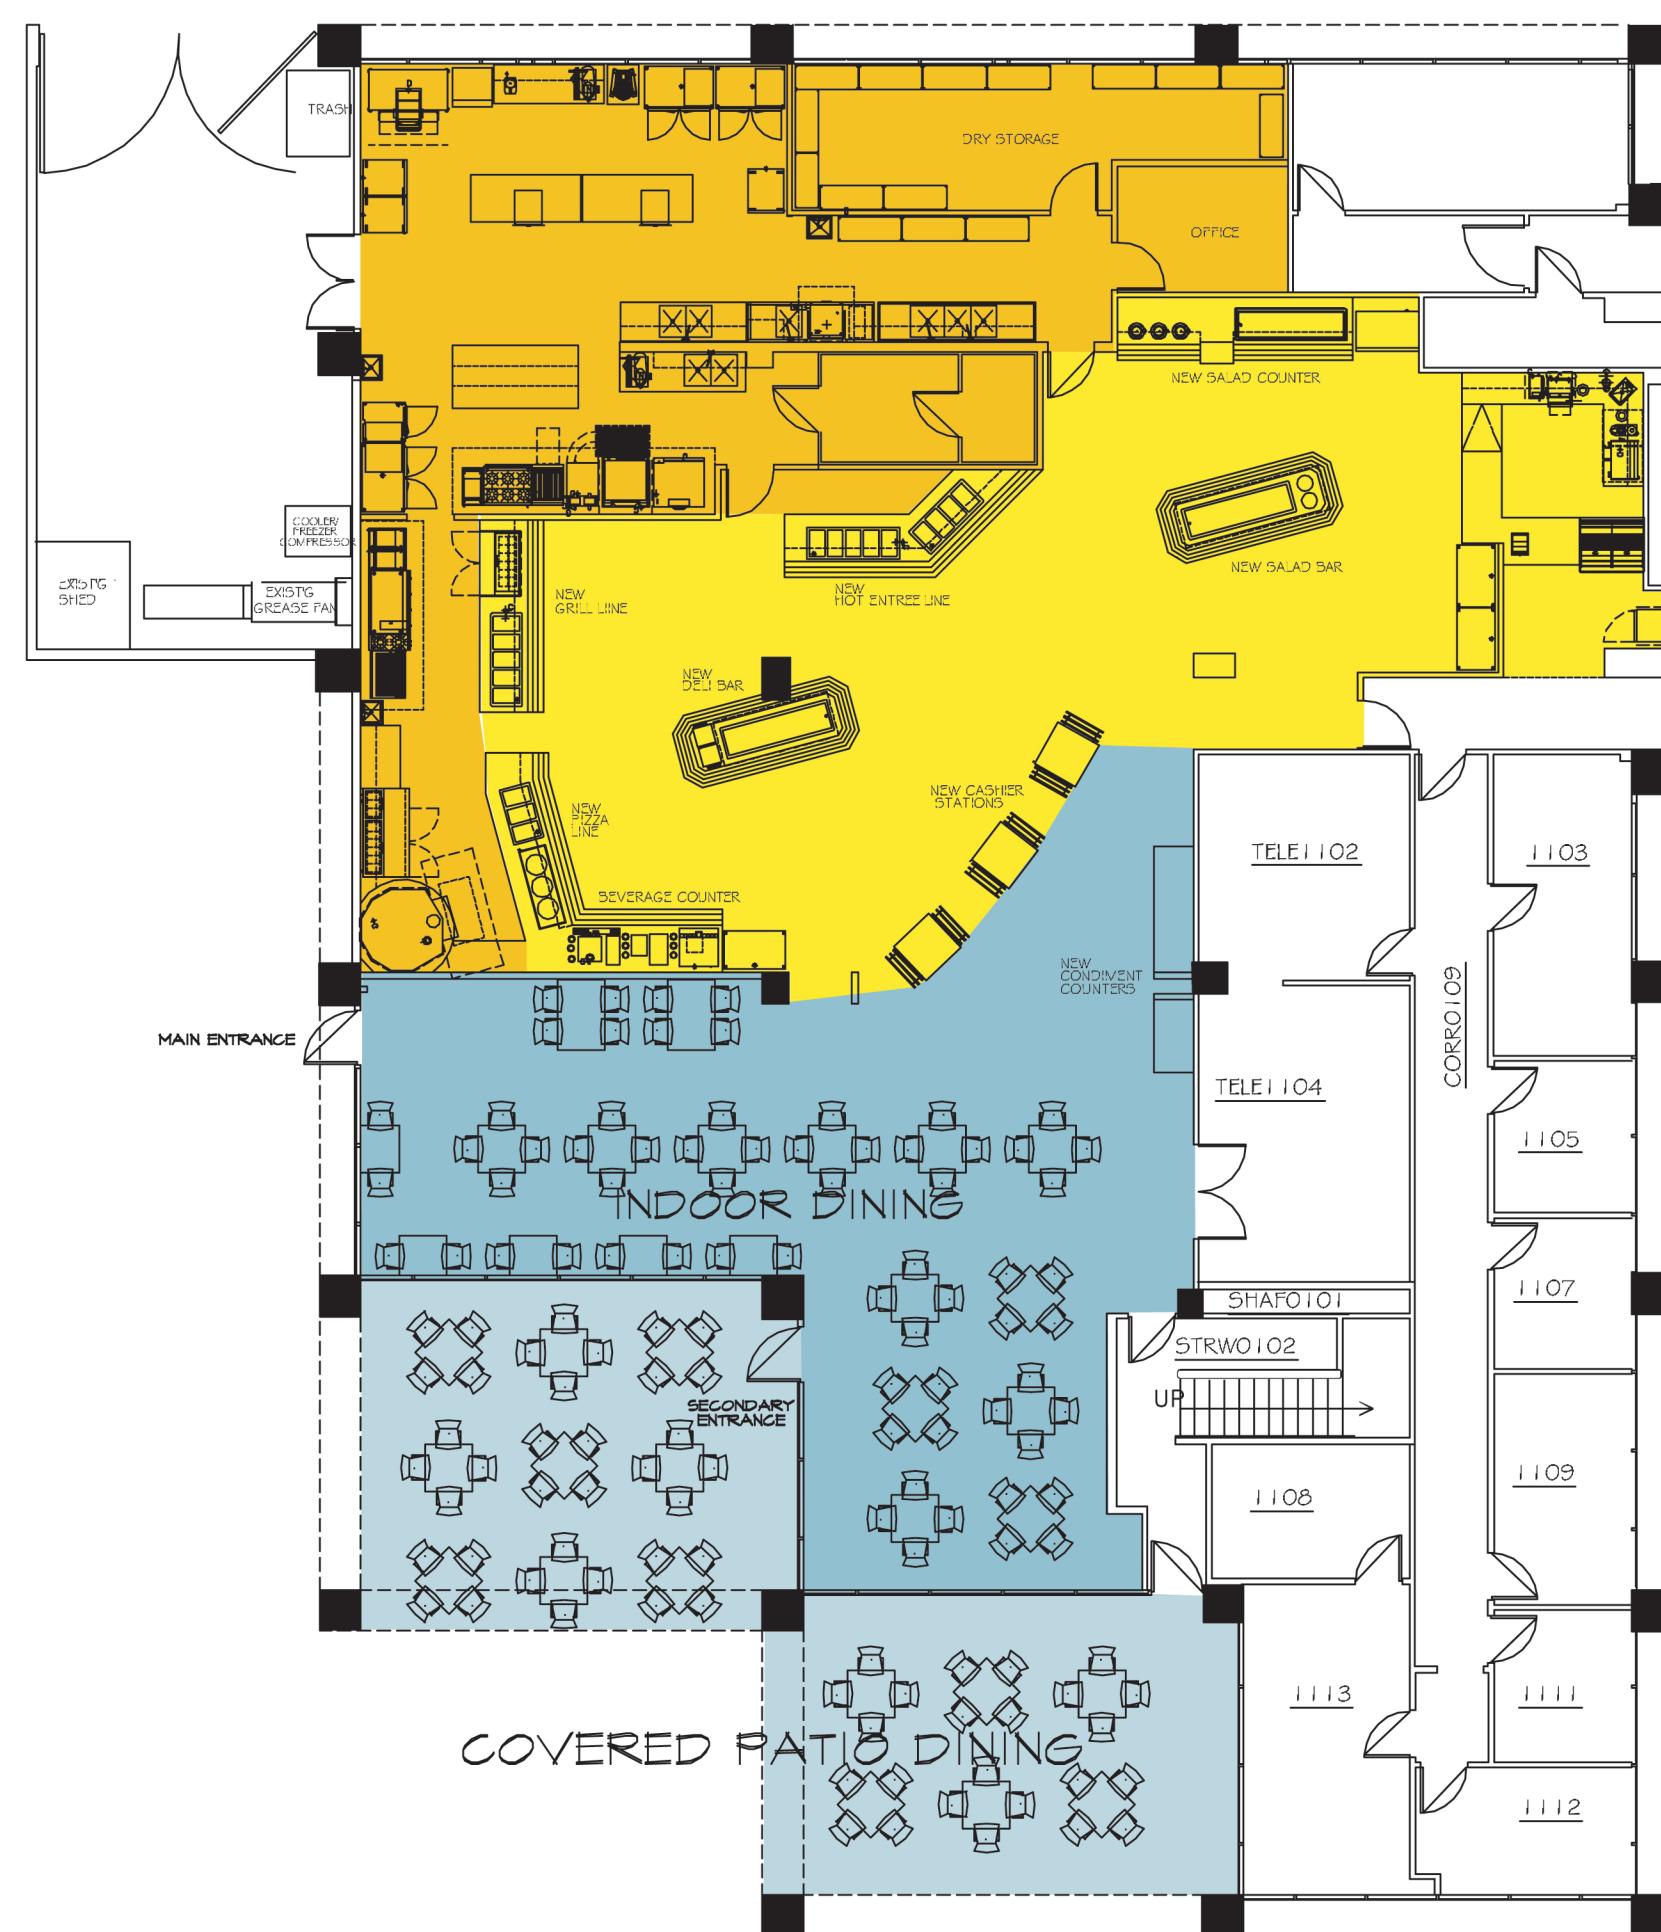

Option I

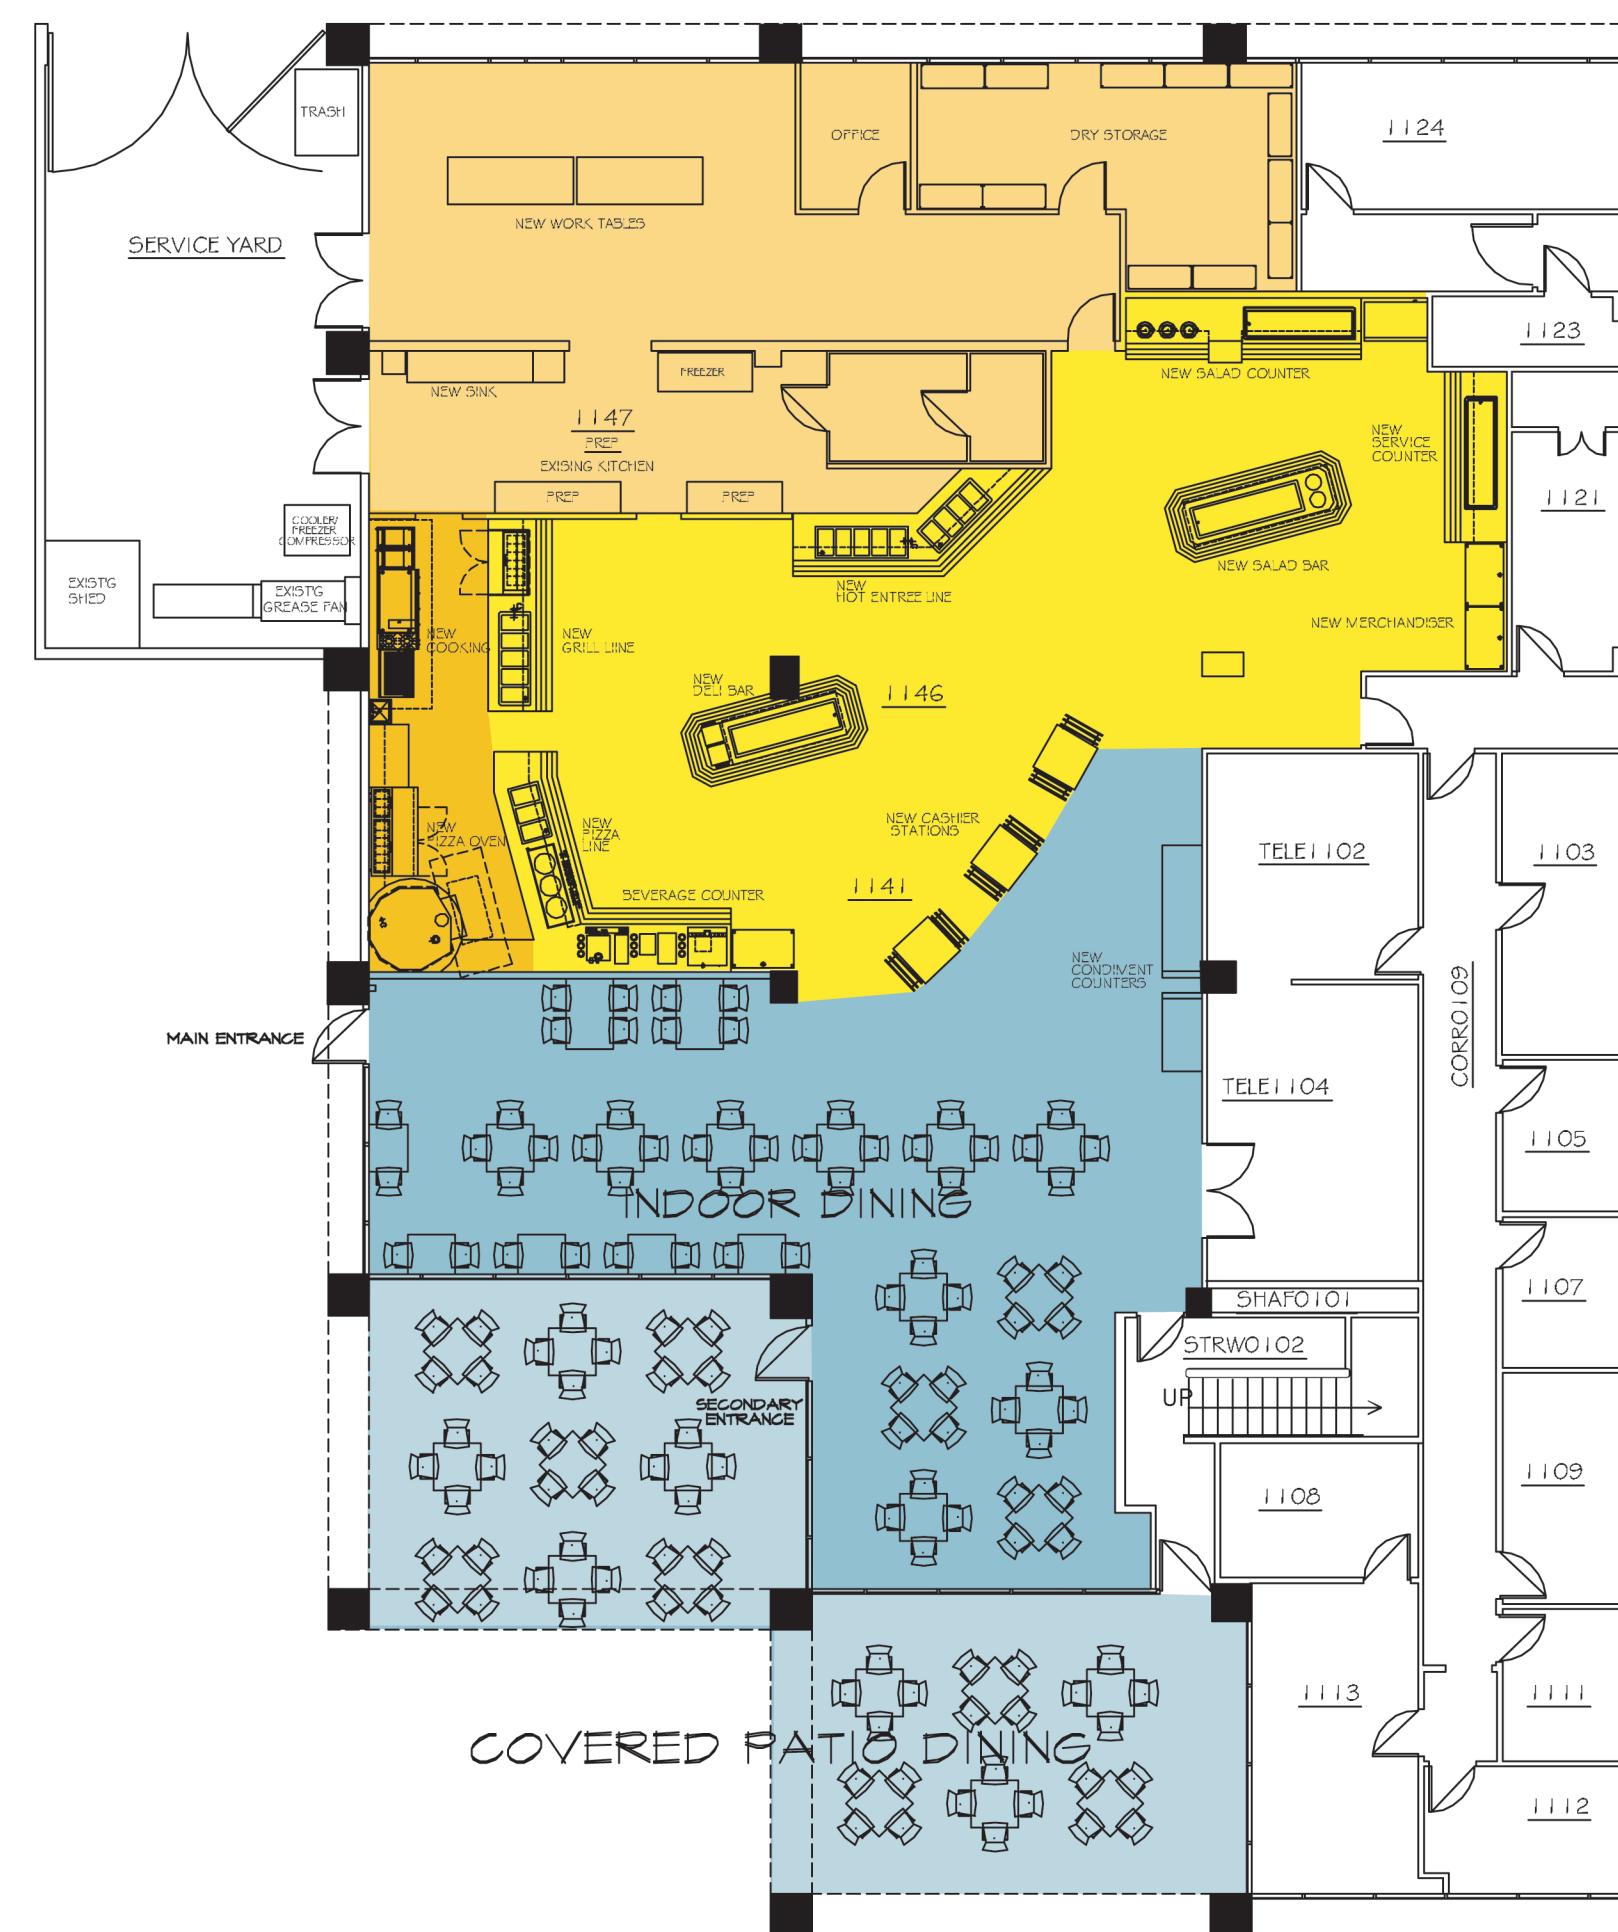

Option II

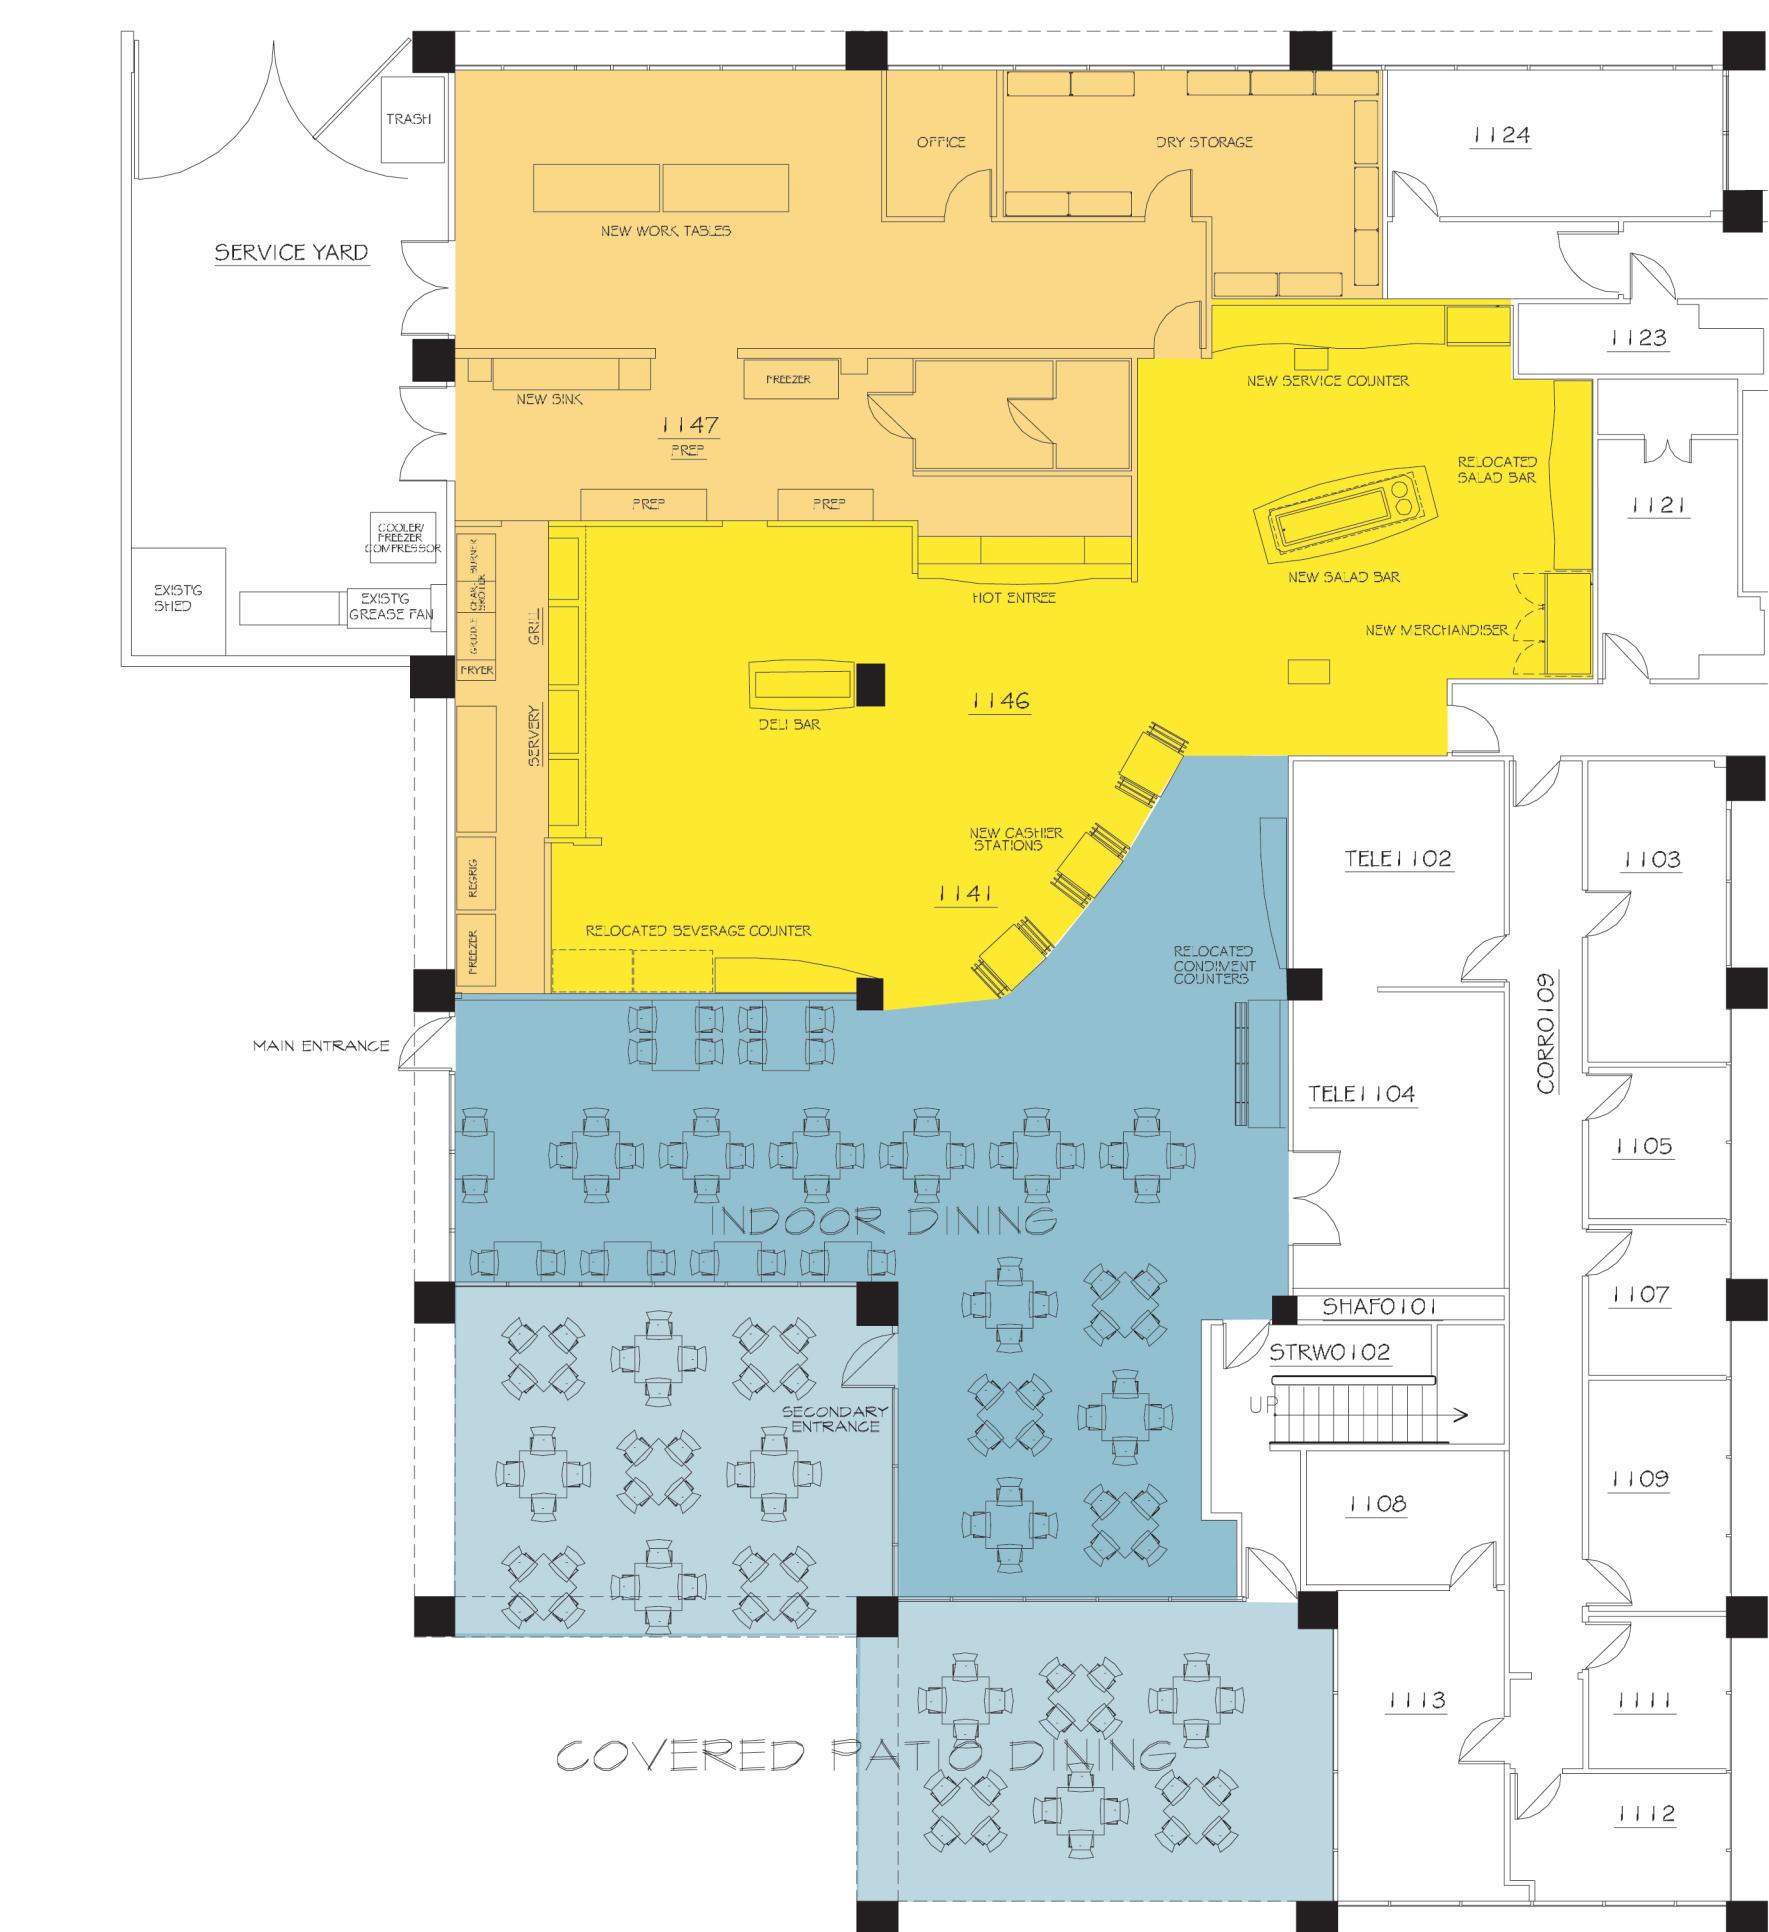

Option III